
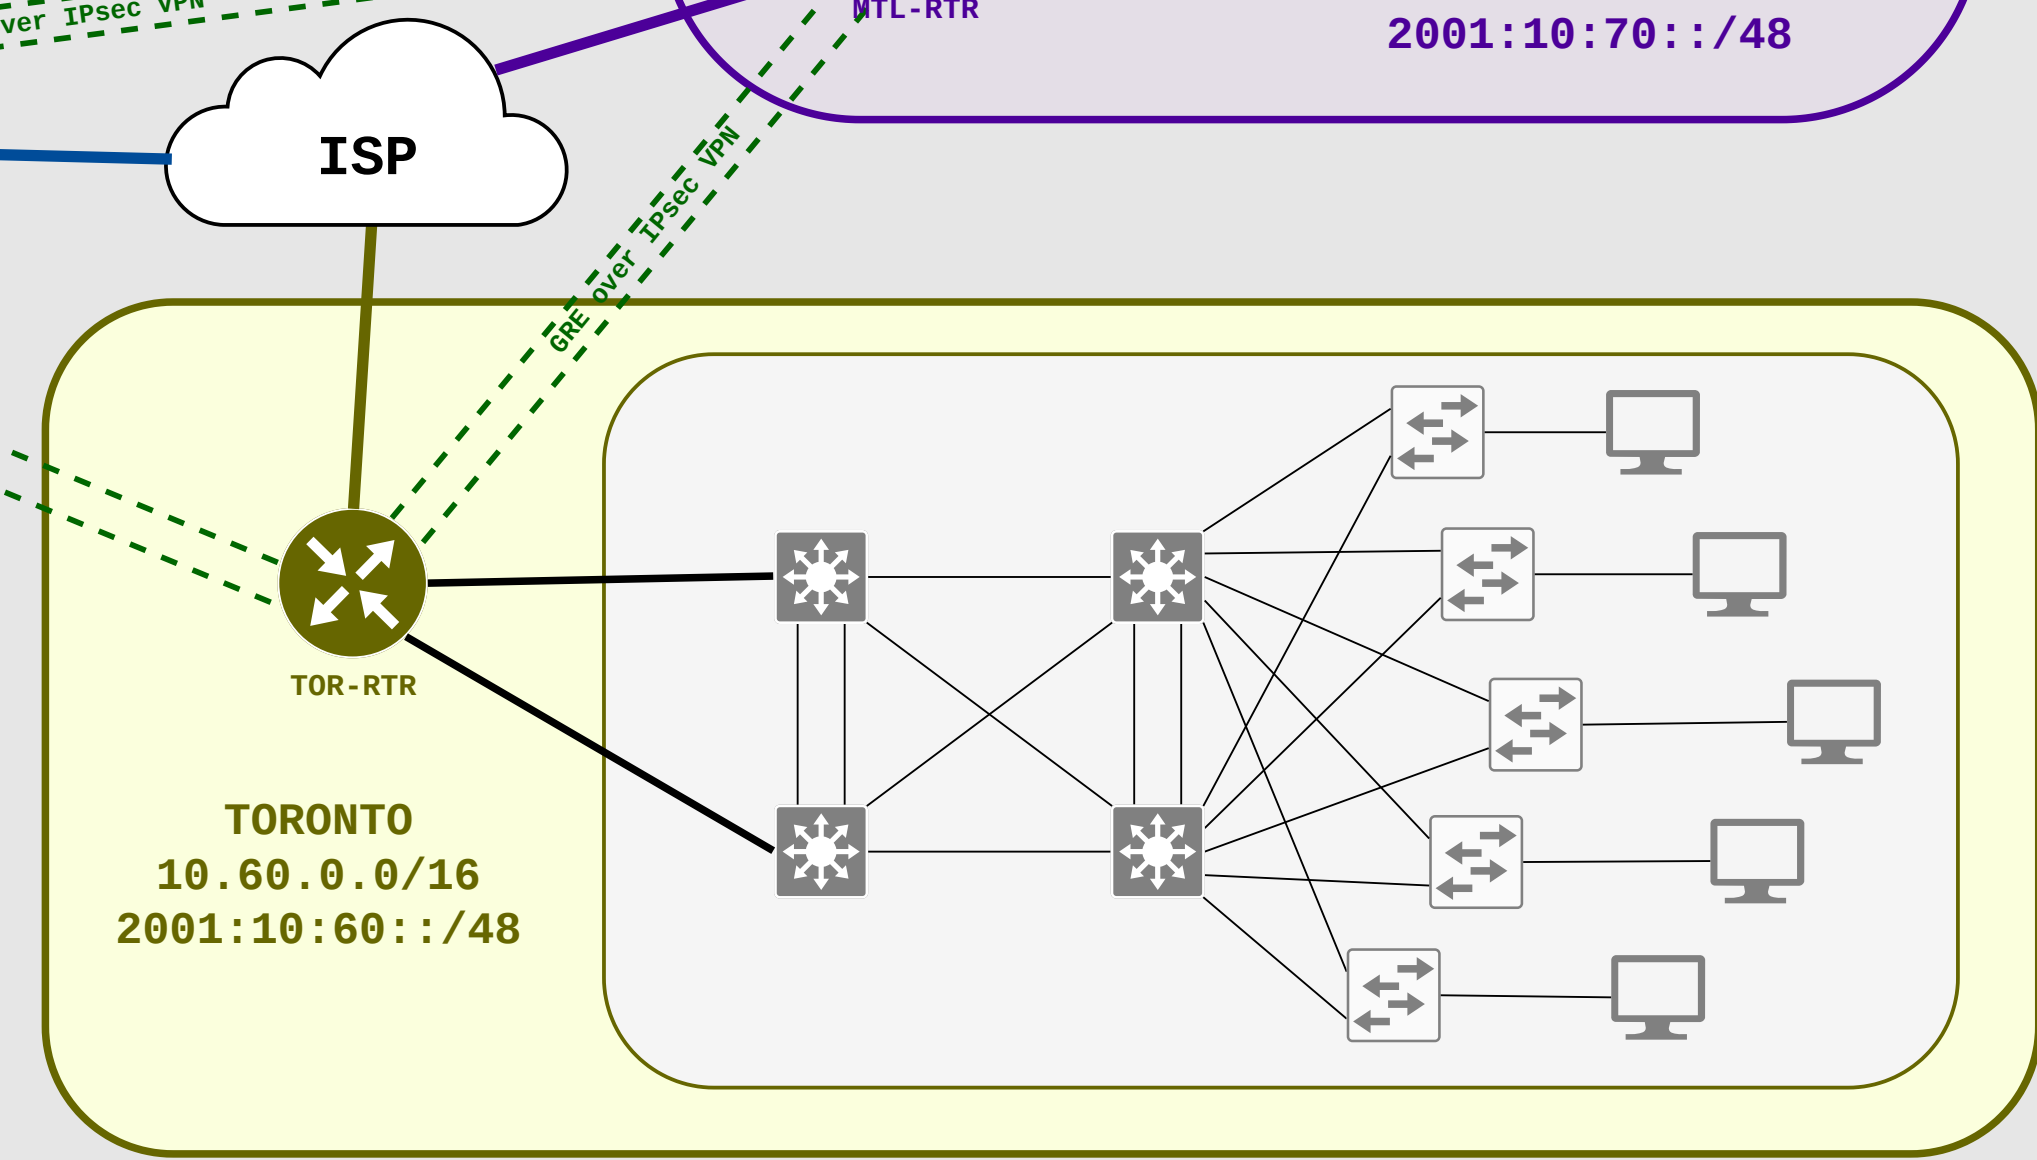
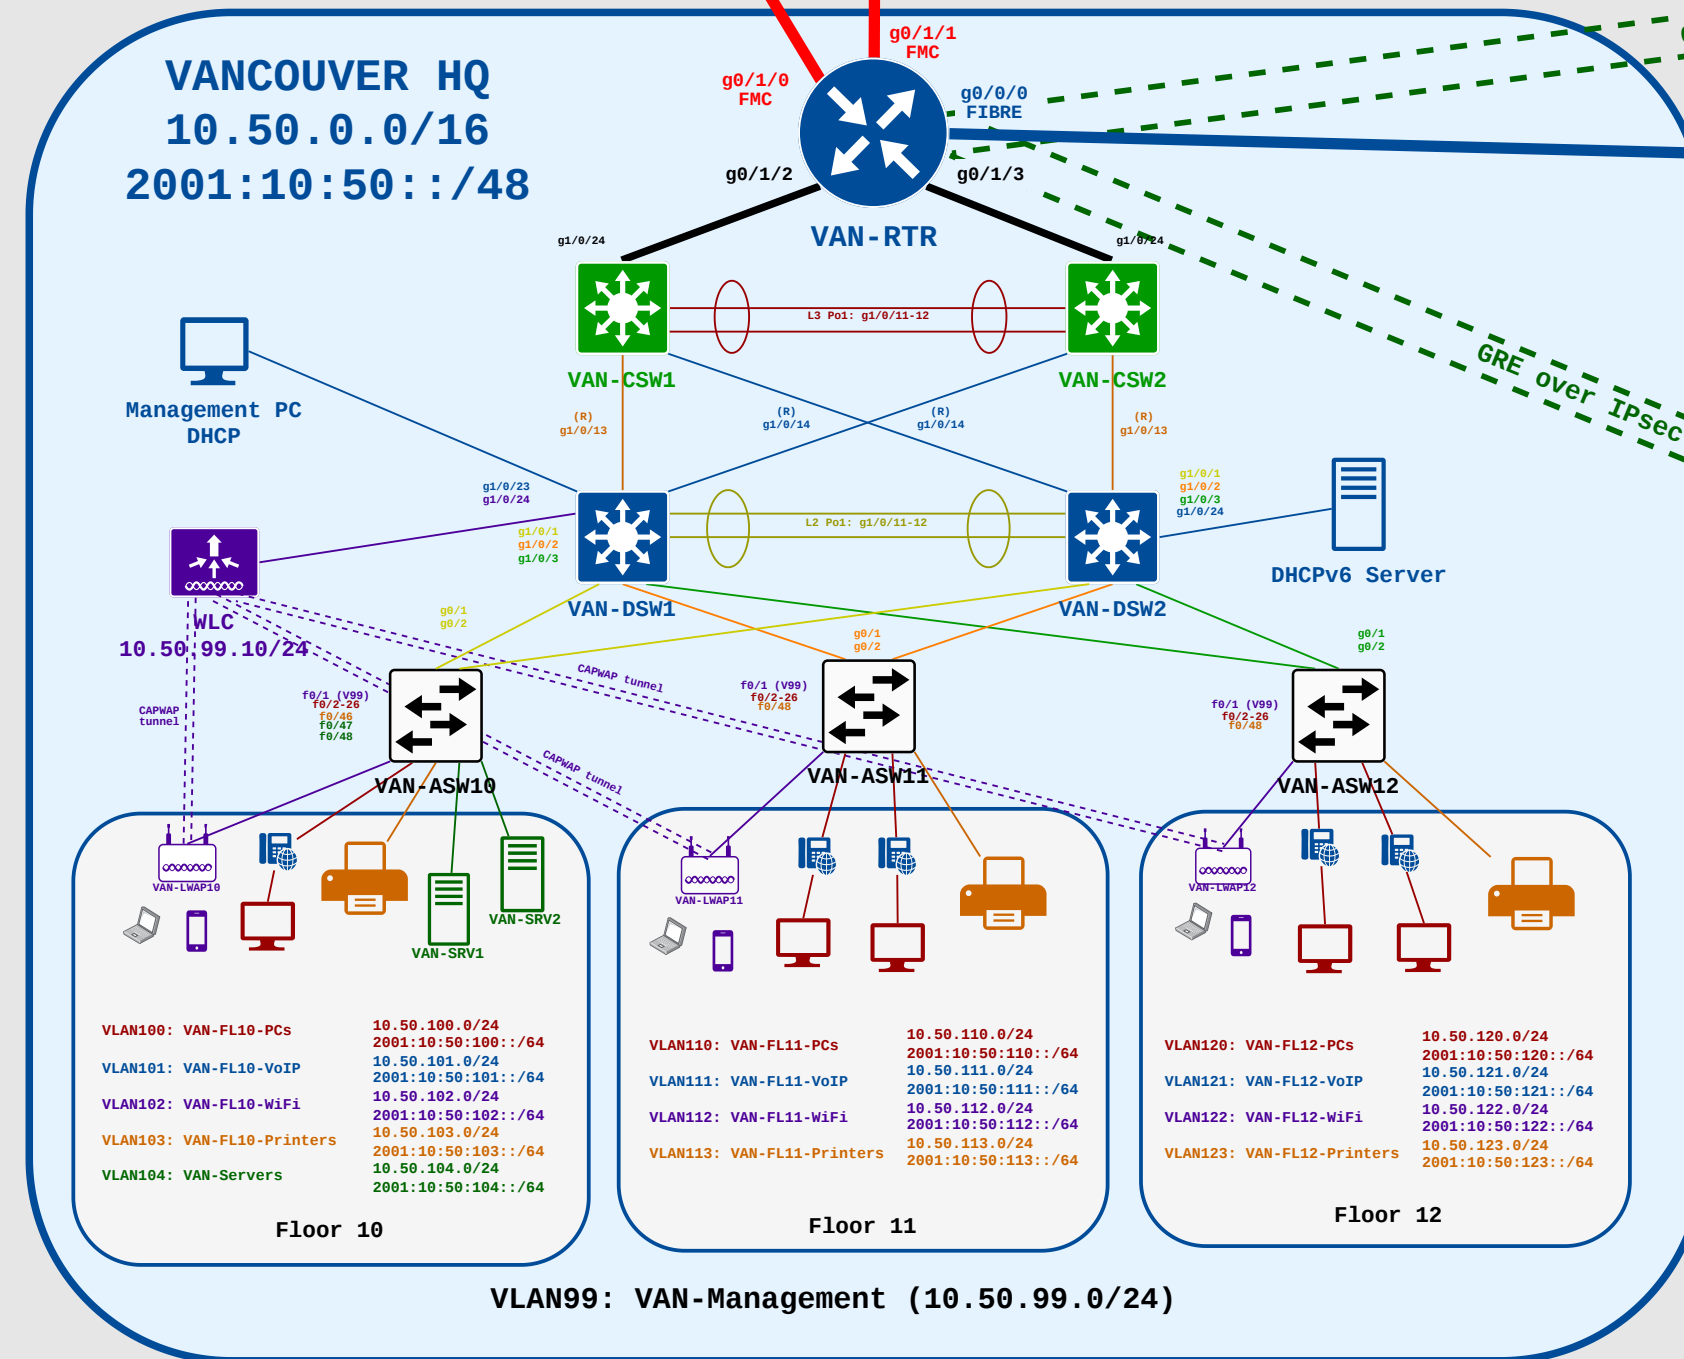
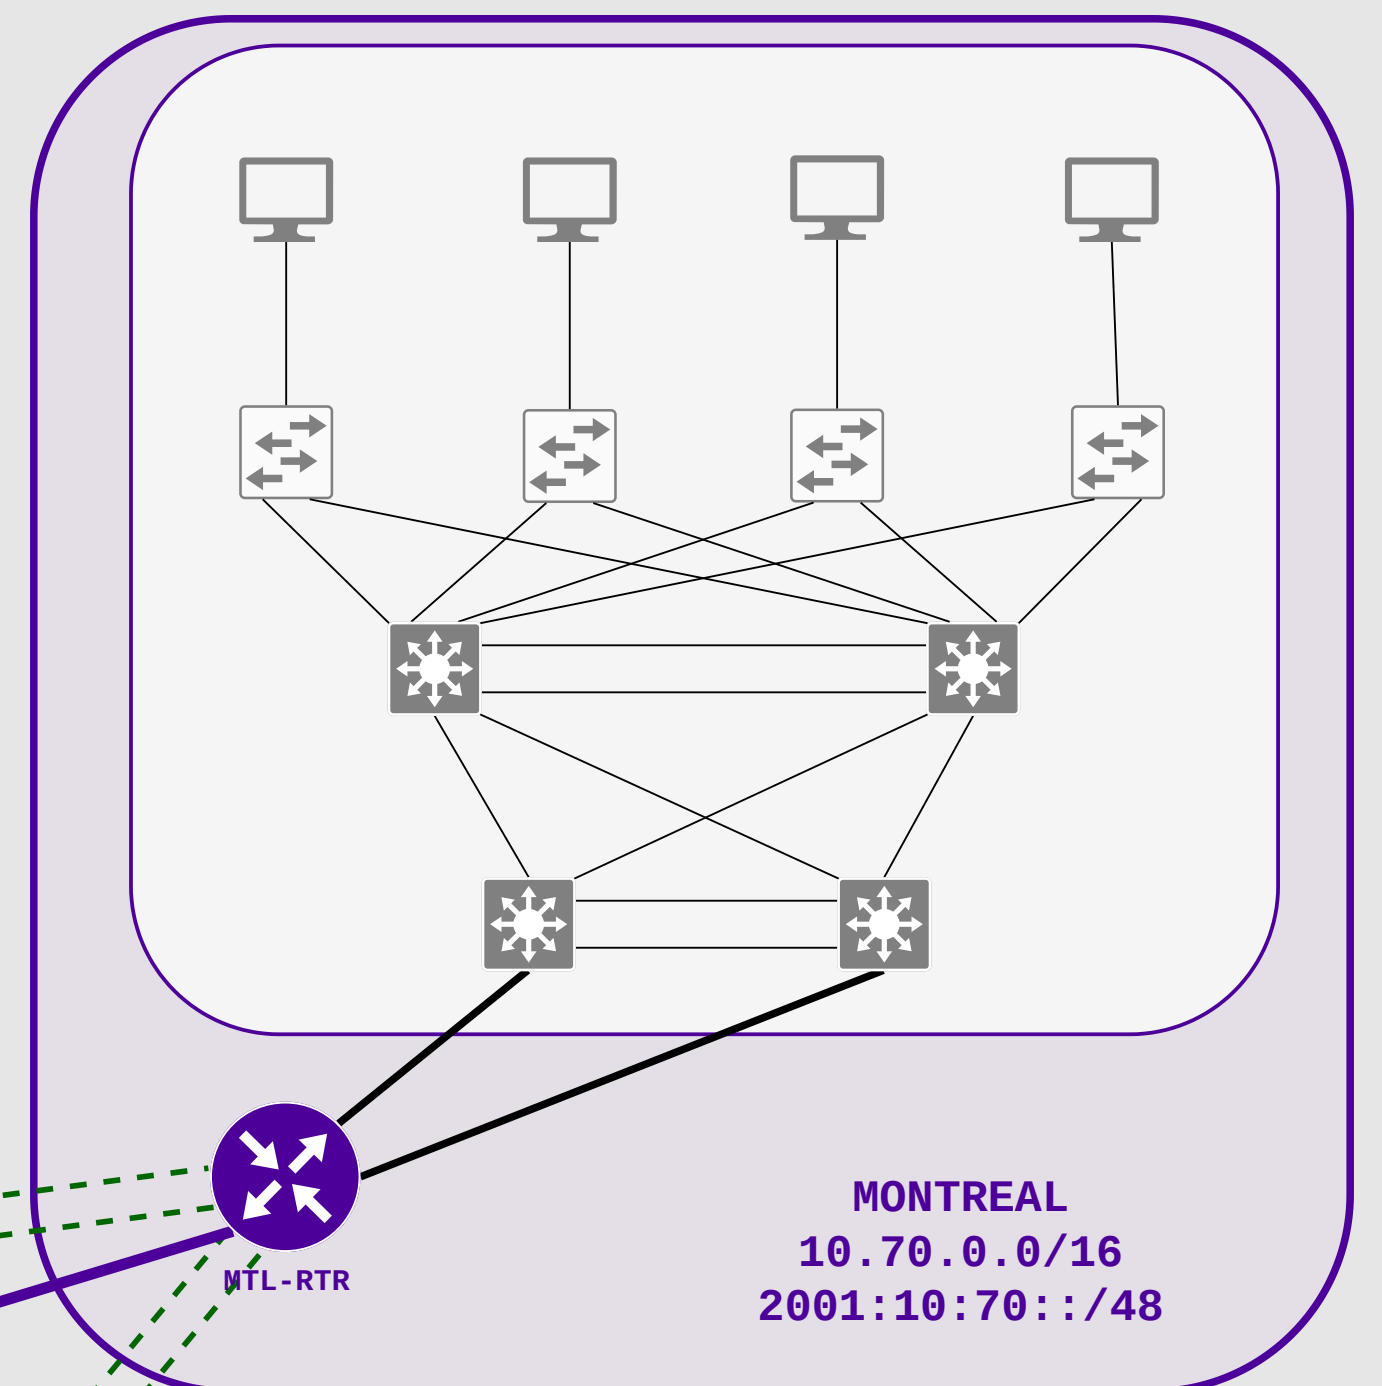
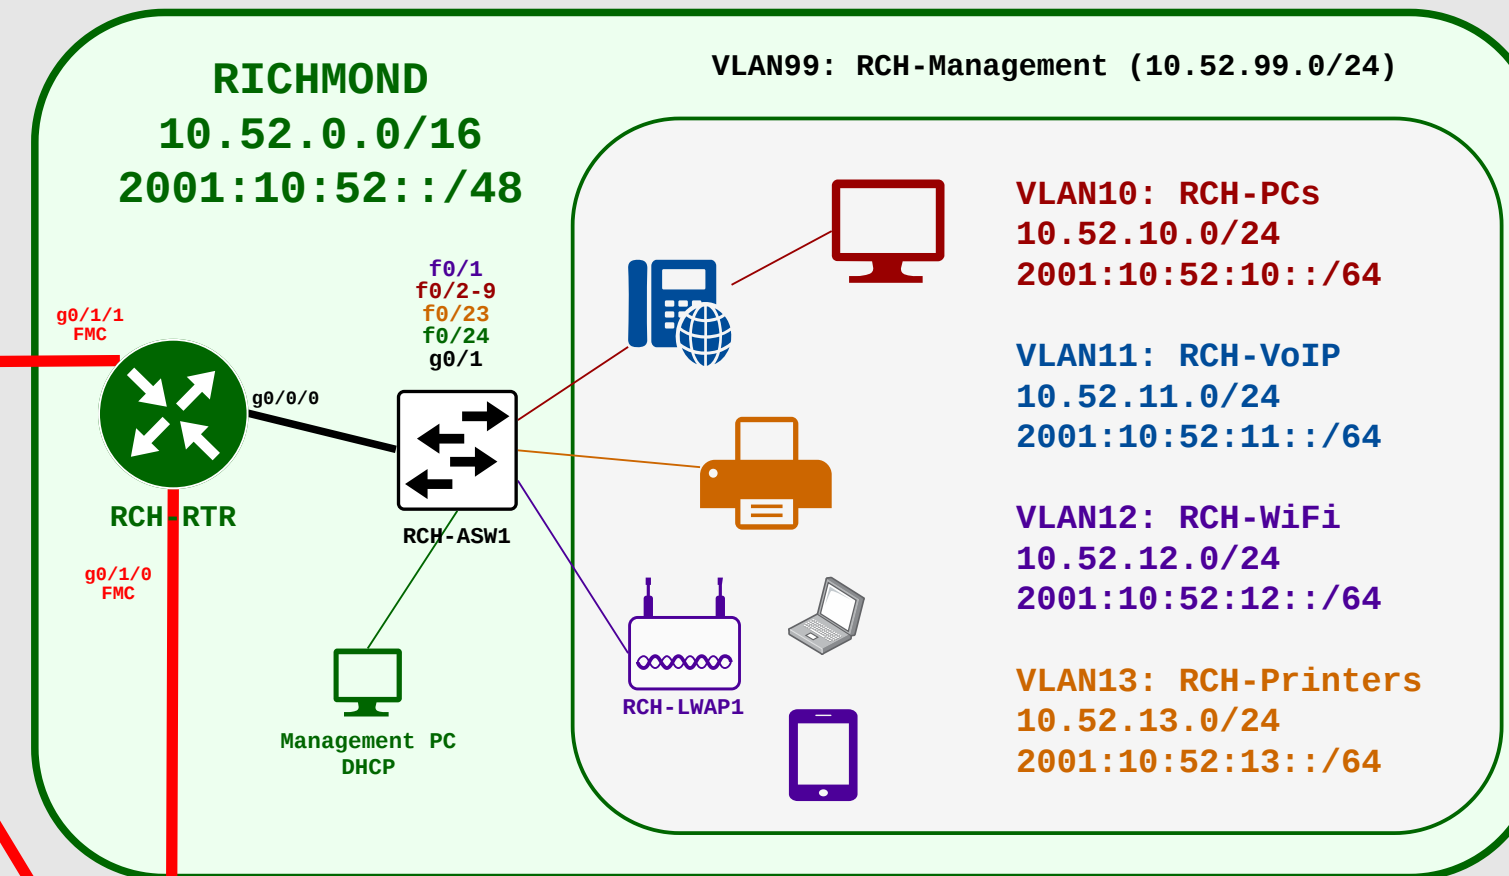


```
speedrun.ccna
20.26.0.0/16
```

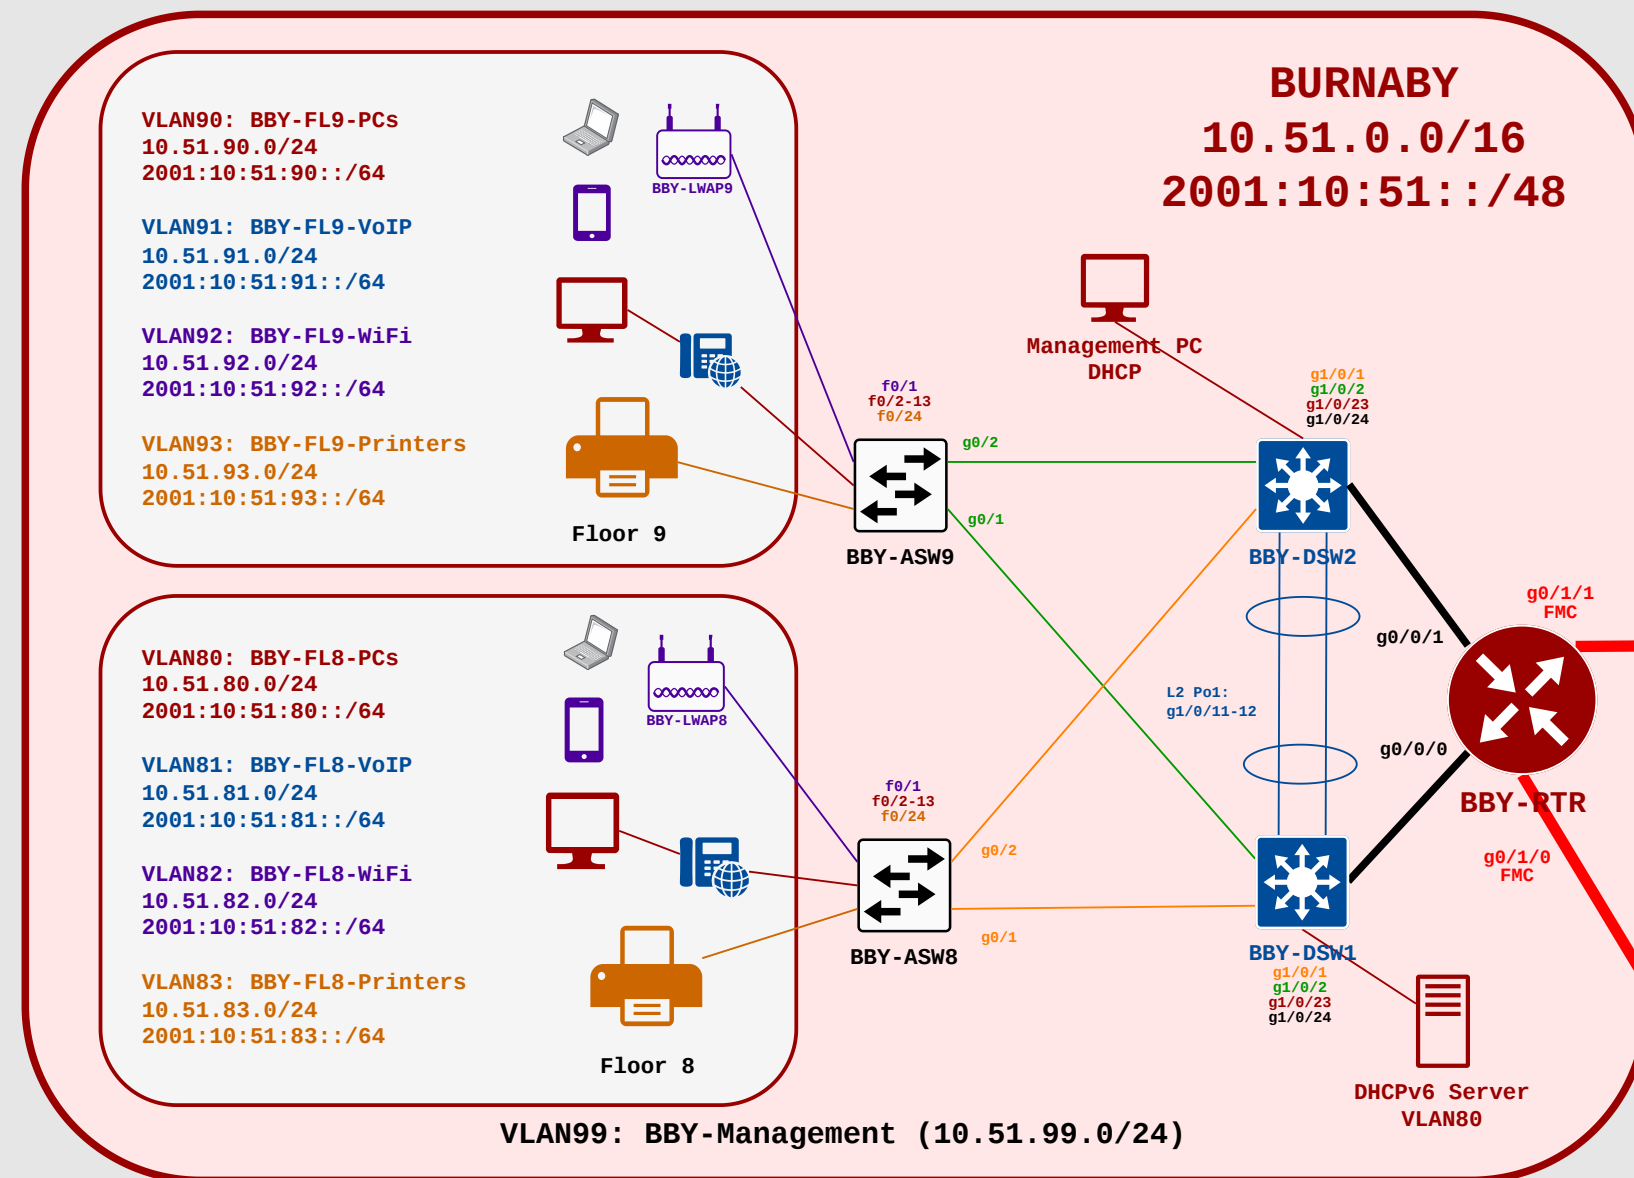

PUBLIC ADDRESS POOLS

Vancouver: 20.26.50.0/25

.....

- Floor10-PCs: 20.26.50.0/27 (Dynamic)
- Floor11-PCs: 20.26.50.32/27 (Dynamic)
- Floor12-PCs: 20.26.50.64/27 (Dynamic)
- Floor10-WiFi: 20.26.50.96/29 (PAT)
- Floor11-WiFi: 20.26.50.104/29 (PAT)
- Floor12-WiFi: 20.26.50.112/29 (PAT)
- VAN-SRV1: 20.26.50.121/32 (Static)

Burnaby: 20.26.50.128/26

.....

- Floor8-PCs: 20.26.50.128/28 (Dynamic)
- Floor9-PCs: 20.26.50.144/28 (Dynamic)
- Floor8-WiFi: 20.26.50.160/30 (PAT)
- Floor9-WiFi: 20.26.50.164/30 (PAT)

Richmond: 20.26.50.192/30

.....

- PCs: 20.26.50.193/32 (PAT)
- WiFi: 20.26.50.194/32 (PAT)

Toronto: 20.26.60.0/24

Montreal: 20.26.70.0/24